


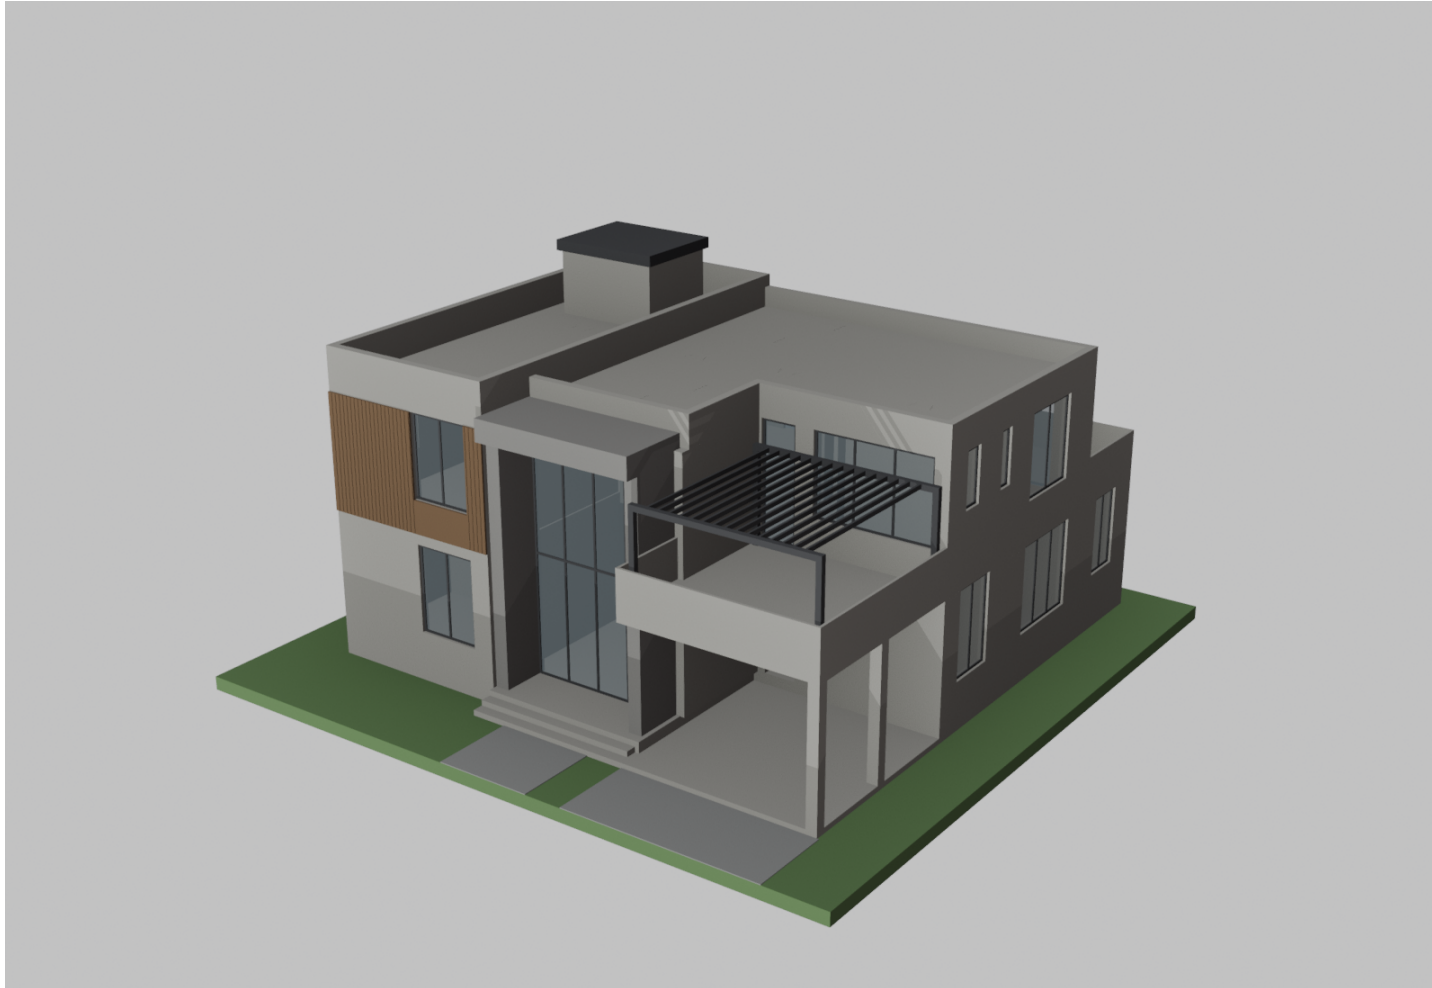

Modern Villa

Display model at 1:37.5

3D printed PETG · lift-off floors

Real footprint 15.20×15.50 m


5 bedrooms · ~ 320 m² over 2 floors

Base 500×500 mm · height 267 mm


Scan for 3D, AR and blueprints:




<https://dgorilla.github.io/moforge-ar/ar/mf-2026-0004-villa/>

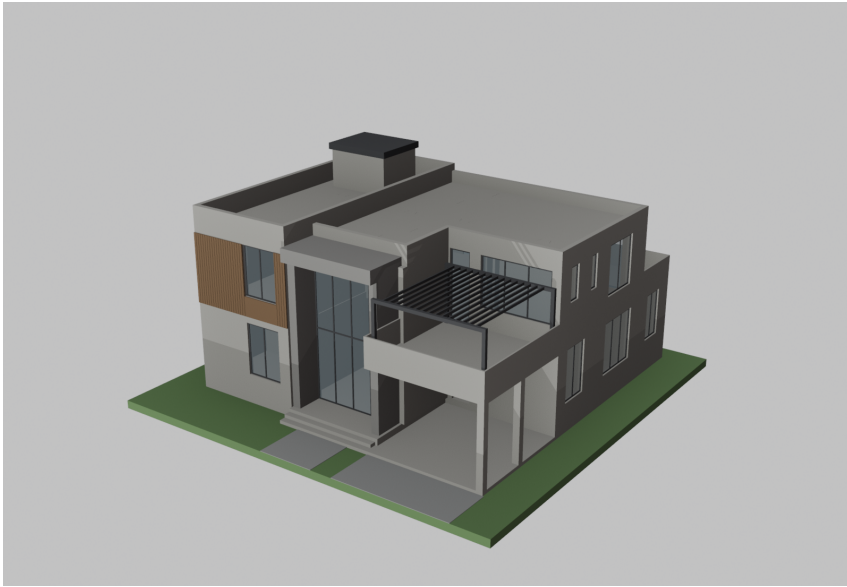


Front

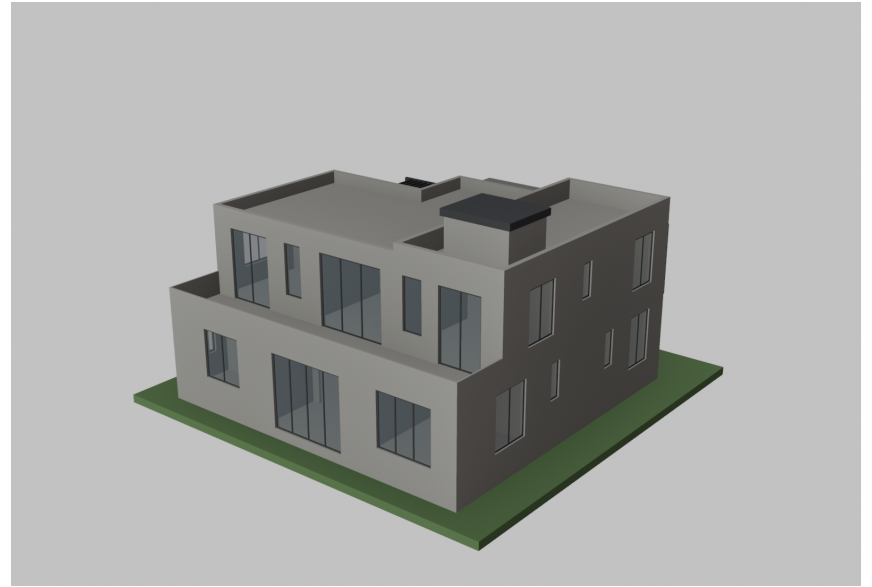

Rear

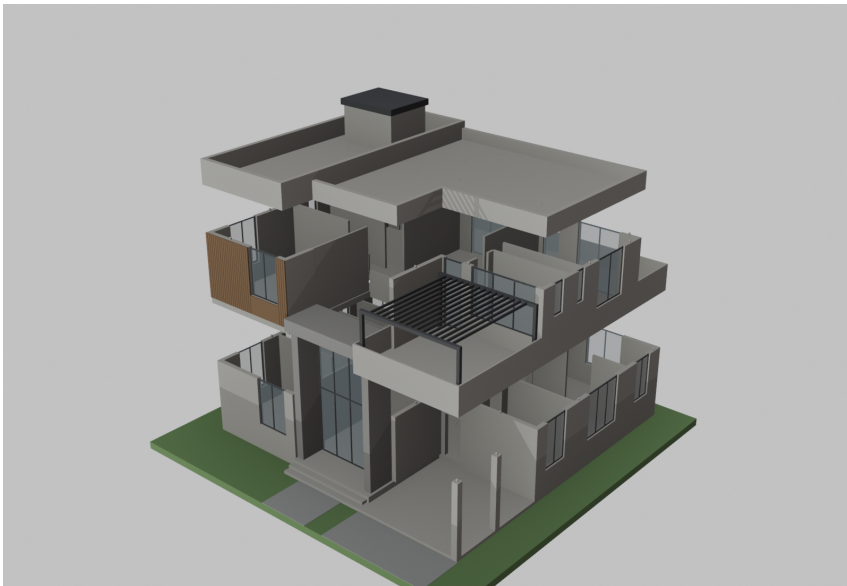


Roof and first floor lifted

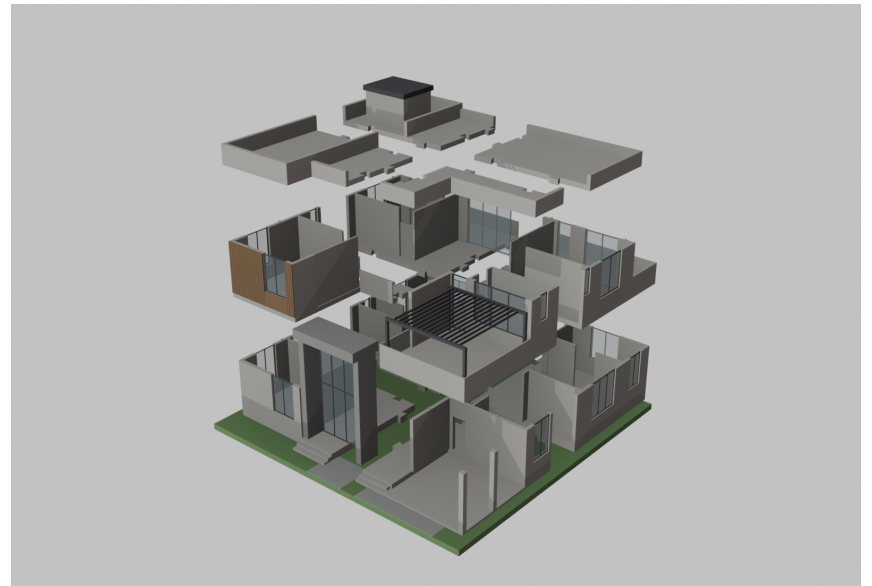

Exploded: 3 levels × 4 tiles



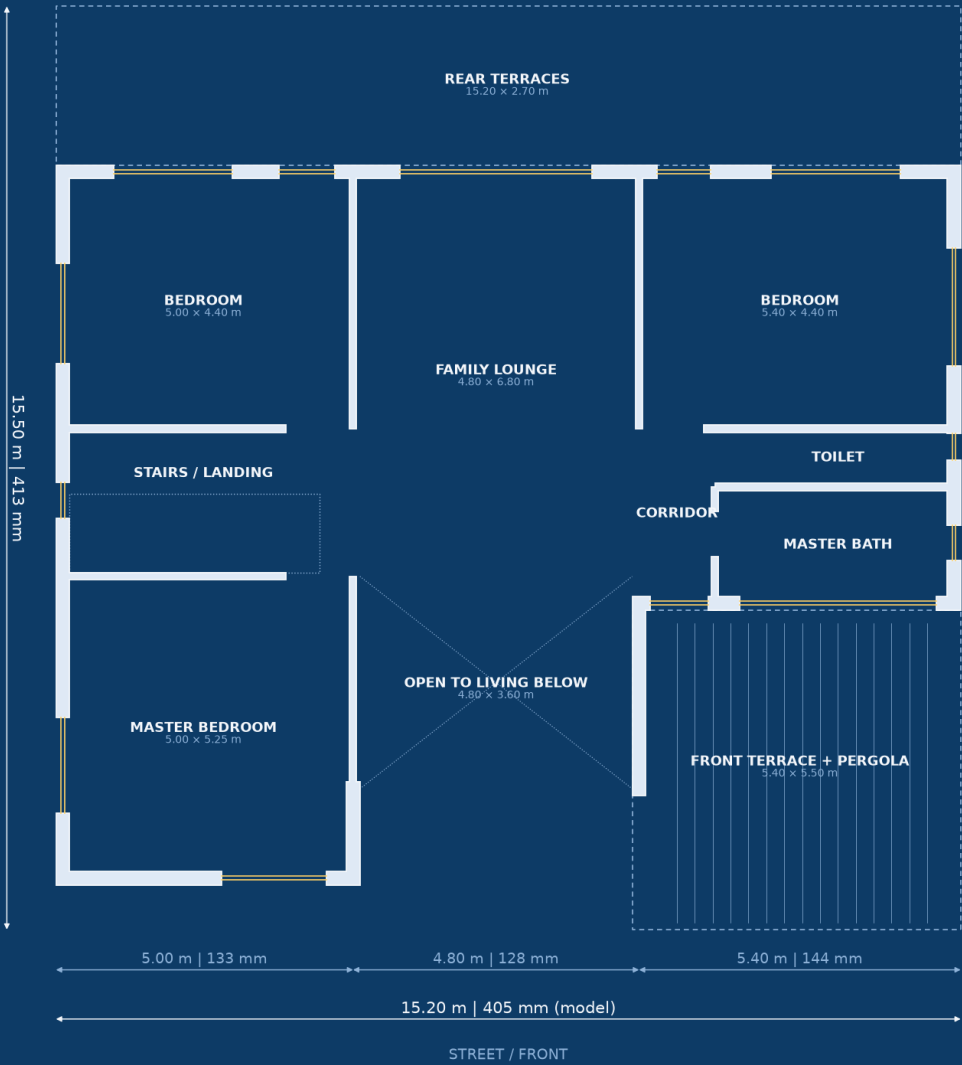

FIRST FLOOR PLAN · scale 1:37.5

MF-2026-0004 · Modern Villa · display model 1:37.5 · model mm / real m · drawn from the print model, 2026-09-28





Scale	1:37.5 (1 m = 26.67 mm)
House	405 × 413 mm on a 500 × 500 × 10 mm board
Height	267 mm board to crown
Walls	6.1 mm exterior · 3.2 mm interior
Levels	ground (plinth + walls) · first (slab + walls) · roof
Split	each level in 4 tiles A–D, dovetail keys, a drop of glue
Lift-off	first floor and roof sit on registration pins: lift to see the rooms
Windows	floor-to-ceiling, drop-in inserts: clear pane + charcoal frame
Material	PETG: ivory, stone grey, charcoal, walnut, clear
Print	Bambu Lab P1S · 0.28 mm layers · no supports

Plate	hours	grams
ground A	5.2	283
ground B	3.9	197
ground C	5.0	280
ground D	4.7	256
first A	3.4	187
first B	3.7	194
first C	4.1	223
first D	4.2	223
roof A	2.5	137
roof B	1.3	67
roof C	2.7	147
roof D	1.8	95
portal stone	3.0	86
charcoal pergola crown	1.6	40
walnut cladding	0.5	13
windows 1 portal glass	1.0	45
windows 2	1.3	60
windows 3	0.7	28
Total · 18 plates	50.6	2563

Assembly

- 1 Glue ground tiles A–D together (dovetails) and onto the painted board.
- 2 Slide the window inserts into their grooves; seat the portal with its glass wall.
- 3 Join first-floor tiles, add cladding and pergola; set it on the pins (no glue).
- 4 Join roof tiles, glue the crown lid; set the roof on the pins (no glue).
- 5 Landscaping (trees, cars, furniture): phase 2.